





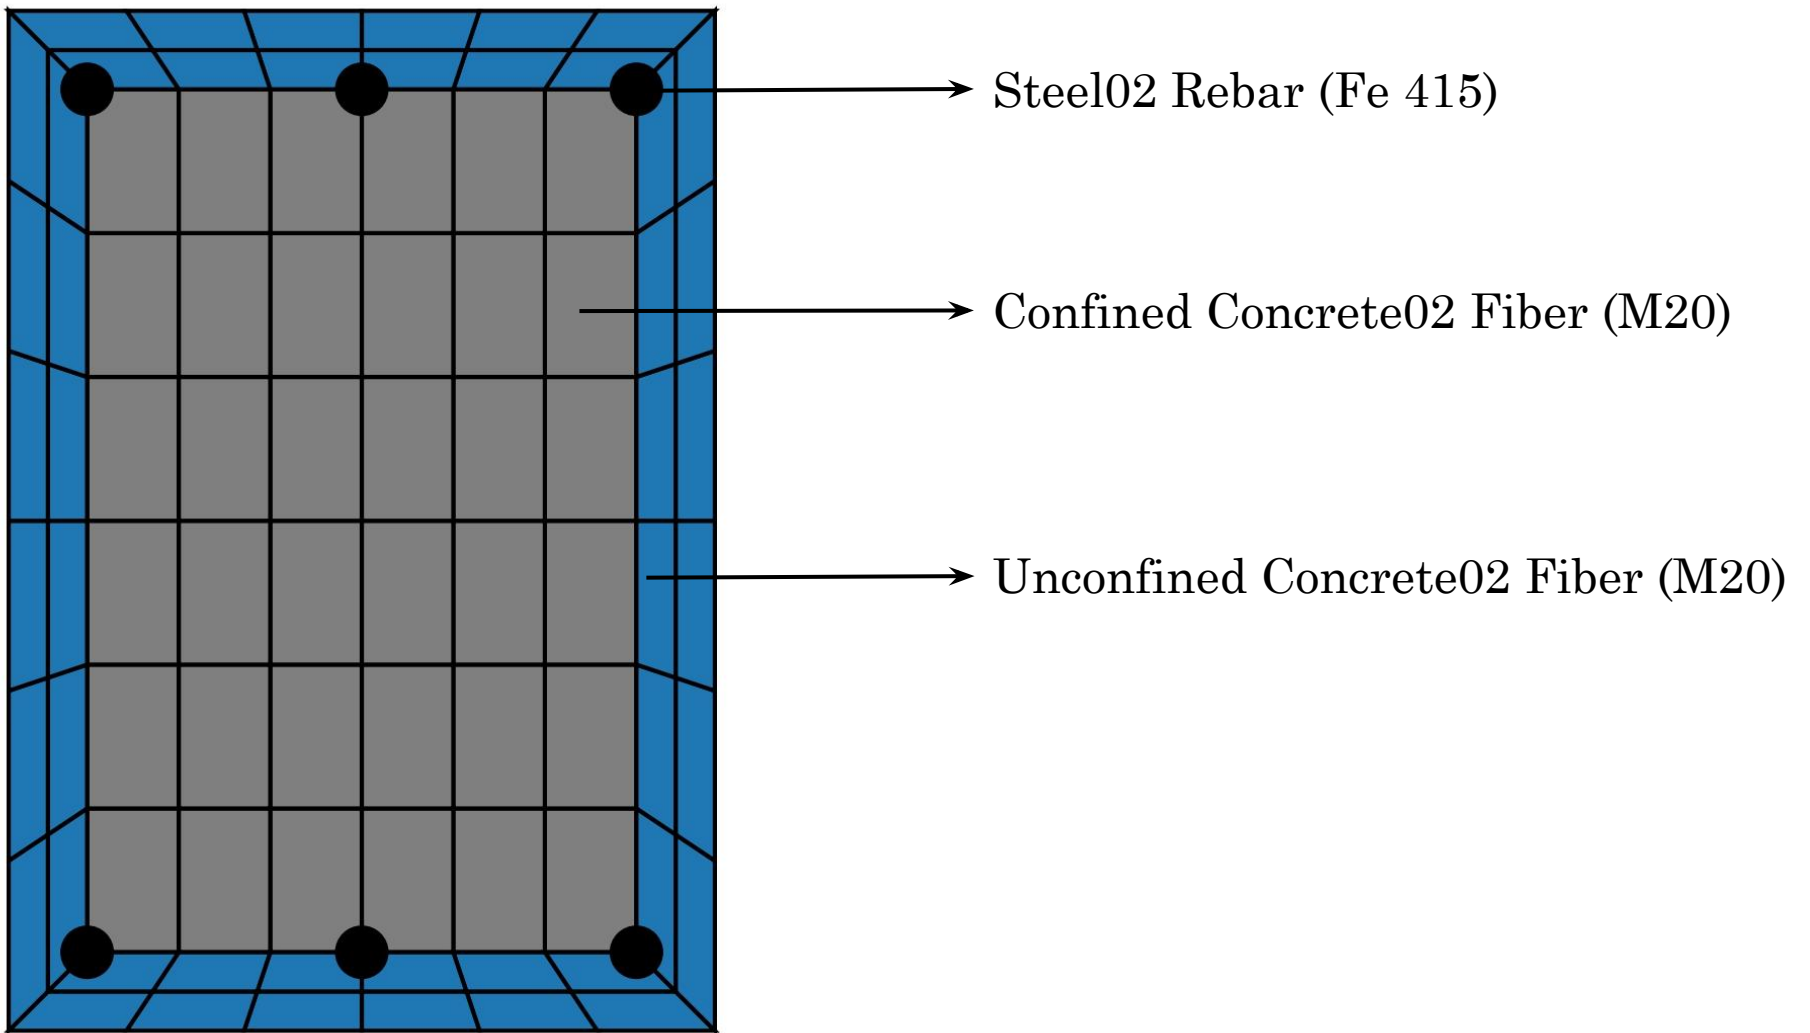

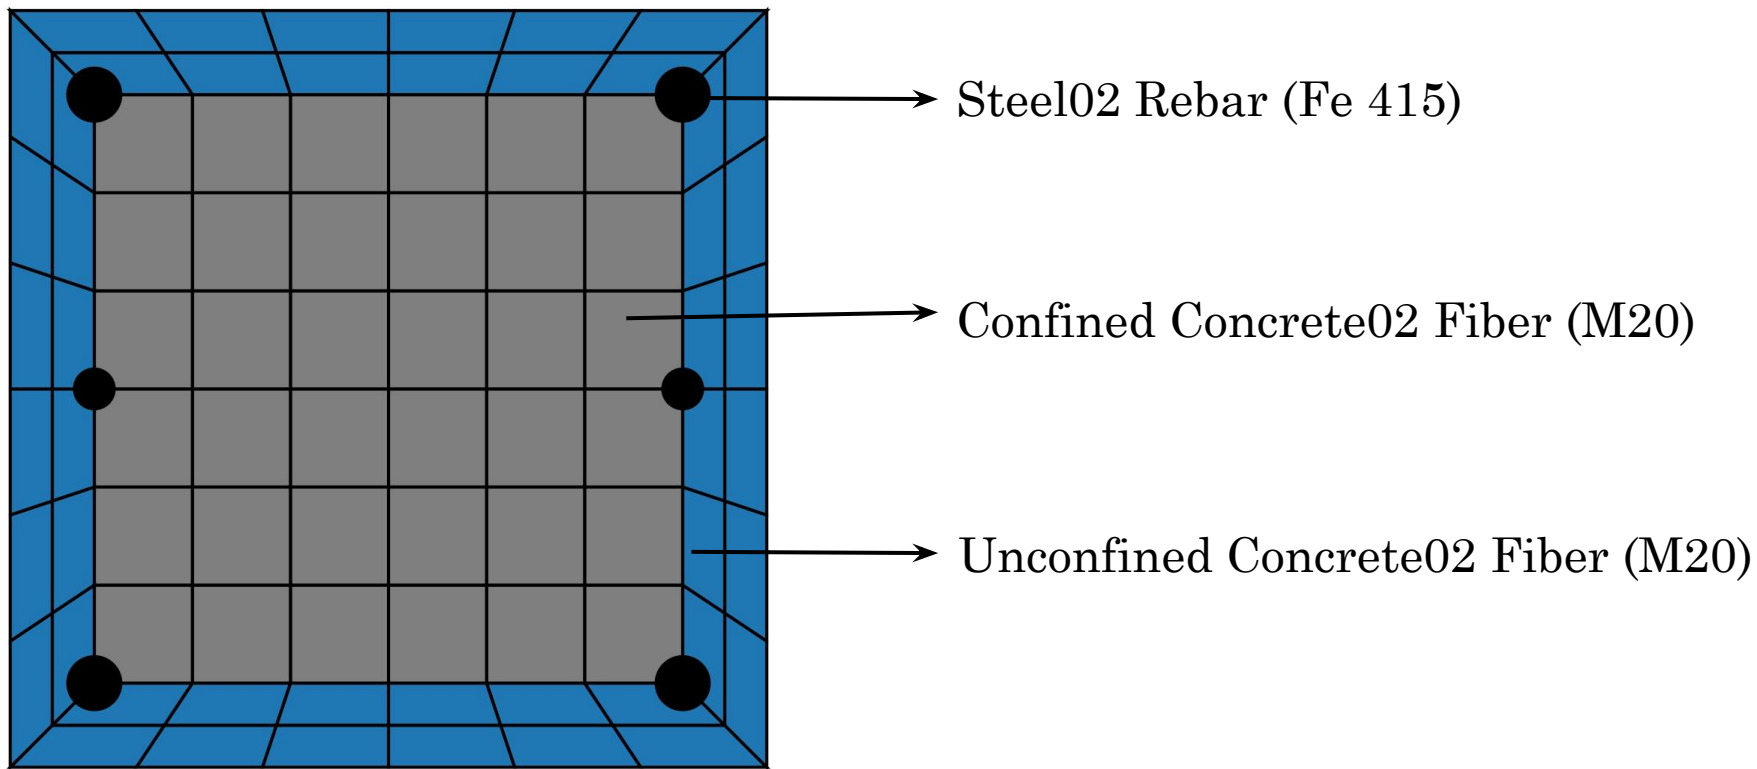

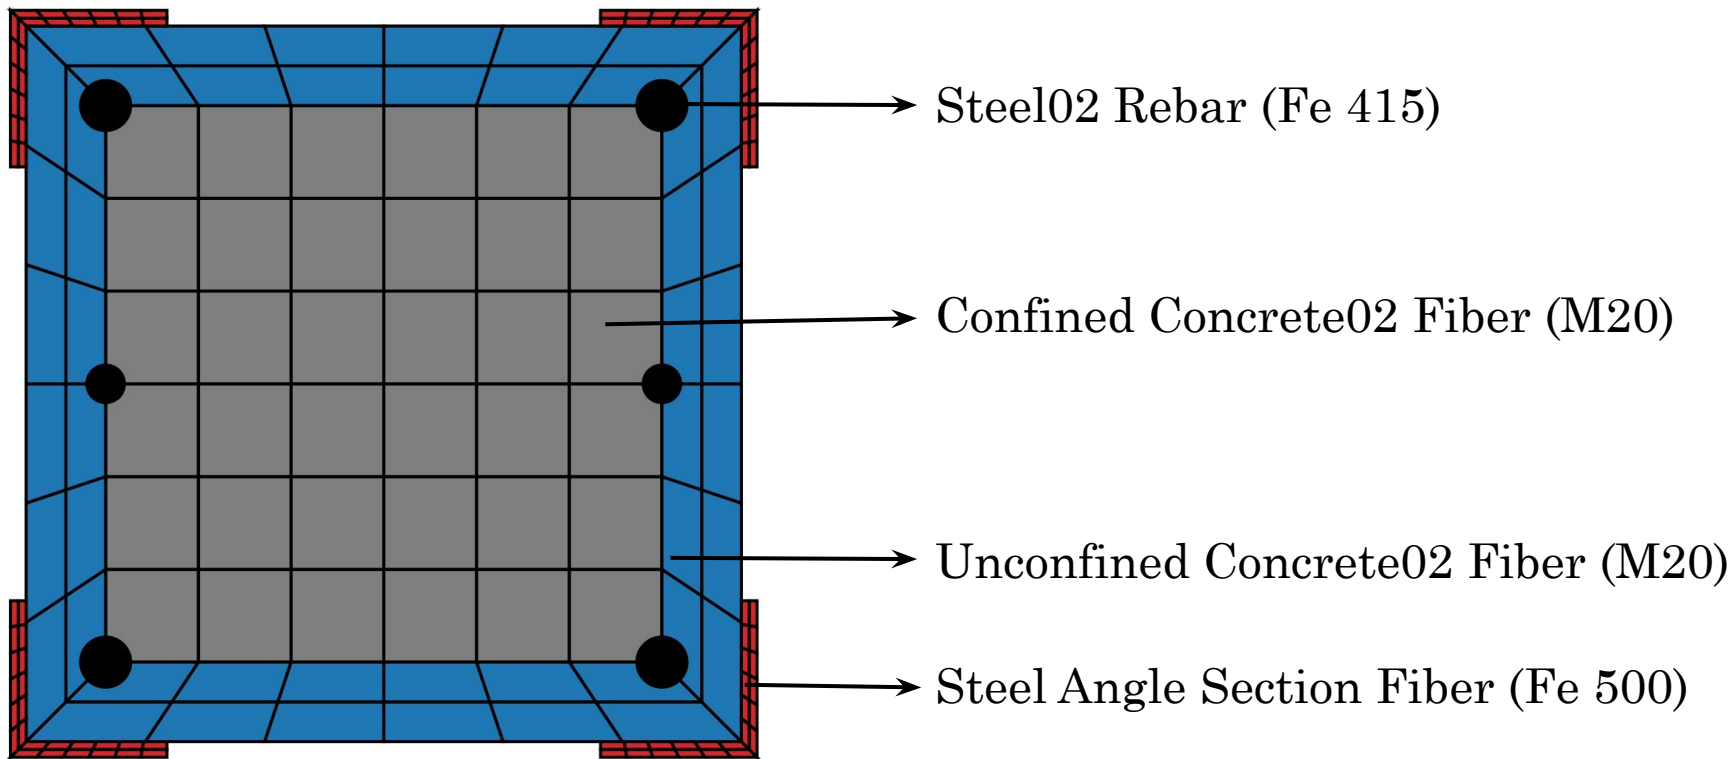

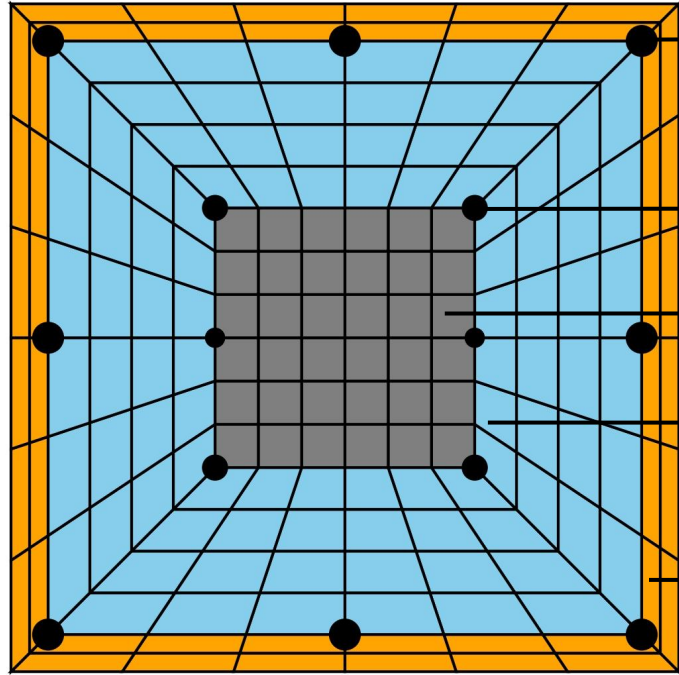

Steel02 Rebar (Fe 500)

Steel02 Rebar (Fe 415)

Existing Confined Concrete02 Fiber (M20)

Jacketed Confined Concrete02 Fiber (M25)

Jacketed Unconfined Concrete02 Fiber (M25)